FIRE HYDRANT DISTANCE

Hydrant 1 to 2	= 90.00m
Hydrant 2 TO 3	= 88.00m
Hydrant 3 TO 4	= 90.00m
Hydrant 4 TO 5	= 50.00m
Hydrant 5 TO 1	= 65.00m

BOMBA LEGEND

NO.	SYMBOL	DESCRIPTION
1	DP	ABC DRY POWDER FIRE EXTIGUISER
2	CO2	CO2 FIRE EXTIGHUISER
3	K	'KELUAR' SIGN
4	EL	EMERGENCY LIGHT
5	HR	HOSE REEL
6	H	FIRE HYDRANT
7	S	SMOKE DETECTOR
8		FIRE ALARM
9		FIRE BREAK
10	H	HEAT DETECTOR
11	FAP	FIRE ALARM PANEL
12		BREECHING INLET
13	EL	EMERGENCY LIGHT (WALL MOUNTED)

LEGEND (FINISHING CODE)

FLOOR FINISHES — FLOOR | WL/COL — WALL/COLUMN FINISHES
CEILING FINISHES — CEILING | SKIRTING — SKIRTING MATERIAL
VENTILATION : — VENTILATION SYSTEM

VENTILATION –
NV – NATURAL VENTILATION
MV – MECHANICAL VENTILATION

WALL FINISHES
PP – 20MM THK. CEMENT PLASTER ON BOTHSIDES & WITH QUALITY EMULSION PAINT INTERNALLY
CT – 20MM THK. CEMENT PLASTER C/W GLAZED CERAMIC TILES UP TO 2400mm HEIGHT FROM FLOOR LEVEL

FLOOR FINISHES
CR – CEMENT RENDER
CT – CERAMIC TILES
PT – POLISHED PORCELAIN TILES
FH – NON METALLIC NATURAL COLOUR HARDENER

SKIRTING FINISHES
CTS – CERAMIC TILES SKIRTING
NS – NO SKIRTING

CEILING FINISHES
PC – GYPSUM BOARD CEILING PANEL
SC – SKIM COAT TO RC. SOFFIT
NC – NO CEILING

DOOR SCHEDULE			WINDOW SCHEDULE		
TYPE	SIZE	DESCRIPTION	TYPE	SIZE	DESCRIPTION
CD1	1500 X 3000	COMPOSITE DOOR WT. ALUMN. ANTI VERMIN NETTING FIXED BESIDE.	W1	2450 X 2000	ALUMN. CASEMENT GLASS WINDOW & FIXED LOUVRED
CD2	2400 X 3000	COMPOSITE DOOR WT. ALUMN. ANTI VERMIN NETTING FIXED BESIDE.	W1a	1250 X 2000	ALUMN. CASEMENT GLASS WINDOW & FIXED LOUVRED
CW1	2100 X 2400	D–LEAF GLASS FLUSH DOOR PART OF CURTAIN GLASS WALL	W2	1560 X 1650	ALUMN. TOP HUNG GLASS WINDOW
D1	1800 X 2100	D–LEAF TIMBER FLUSH DOOR	W4	2300 X 1650	ALUMN. TOP HUNG GLASS WINDOW
D2	1000 X 2100	S–LEAF TIMBER FLUSH DOOR	W5	600 X 450	ALUMN. TOP HUNG GLASS WINDOW
D3	830 X 2100	S–LEAF STEEL PANEL TOILET DOOR	W5a	1200 X 450	ALUMN. TOP HUNG GLASS WINDOW
D4	750 X 2100	S–LEAF TIMBER FLUSH TOILET DOOR	W5b	2400 X 450	ALUMN. TOP HUNG GLASS WINDOW
D5	750 X 2100	S–LEAF TIMBER FLUSH TOILET DOOR	W6	850 X 1550	ALUMN. TOP HUNG GLASS WINDOW
D6	1000 X 2100	S–LEAF STEEL DOOR	W7	750 X 1500	ALUMN. CASEMENT WINDOW
FD–1	1000 X 2100	S–LEAF 1–HR RATED FIRE DOOR	W8	600 X 1200	ALUMN. CASEMENT GLASS WINDOW
GD1	750 X 2100	S–LEAF ALUMN. FRAME GLASS FLUSH DOOR	W9	1200 X 1200	ALUMN. D–LEAF GLASS SLIDING WINDOW
RS1	2100 X 2850	GS ROLLER SHUTTER DOOR	W11	1300 X 1250	ALUMN. TOP HUNG GALSS WINDOW
RS2	7493 X 5000	GS ROLLER SHUTTER DOOR (ELE. OPERATED)	W12	2400 X 1650	ALUMN. TOP HUNG GALSS WINDOW
RS3	8500 X 5000	GS ROLLER SHUTTER DOOR (ELE. OPERATED)	W13	2400 X 1325	ALUMN. TOP HUNG GLASS WINDOW
SD–1	7000 X 5000	M.S. SLIDING DOOR WT. 1.2M X 2.4M DOOR S–LEAF FIRE ESCAPE DOOR TO MANUFS. DETAIL	W14	2400 X 1650	ALUMN. CASEMENT GLASS WINDOW
SD5	1000 X 2100	TIMBER SLIDING DOOR (OKU TOILET)	TW4	2400 X 760	ALUMN. FIXED LOUVRED WINDOW
SG1	900 X 1700	GS SWING GATE	VB1	1585 x 550	VENTILATION BLOCK WINDOW WITH ALUMN. WITH ALUMN. ANTI VERMIN NETTING SIDE.
SG2	4200 X 2100	GS SWING GATE TO T.N.B.'S SPECIFICATION	L1	750 X 365	ALUMN. FIXED LOUVRED WITH 10# ROD AND ANTI VERMIN NETTING
SG3	15000 X 1850	MS MOTORISED SLIDING GATE			

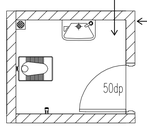

TYPICAL TOILET DETAIL

SCALE 1:50

Notes :

1) Apply to Groundfloor, firstfloor and secondfloor level Toilet
2) Toilet Dimension can refer to layout drawing

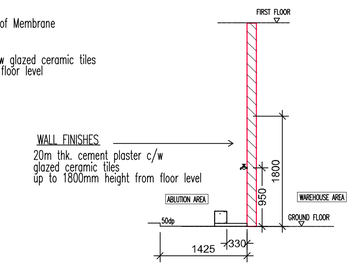

ABLUTION DETAIL

SCALE 1:50

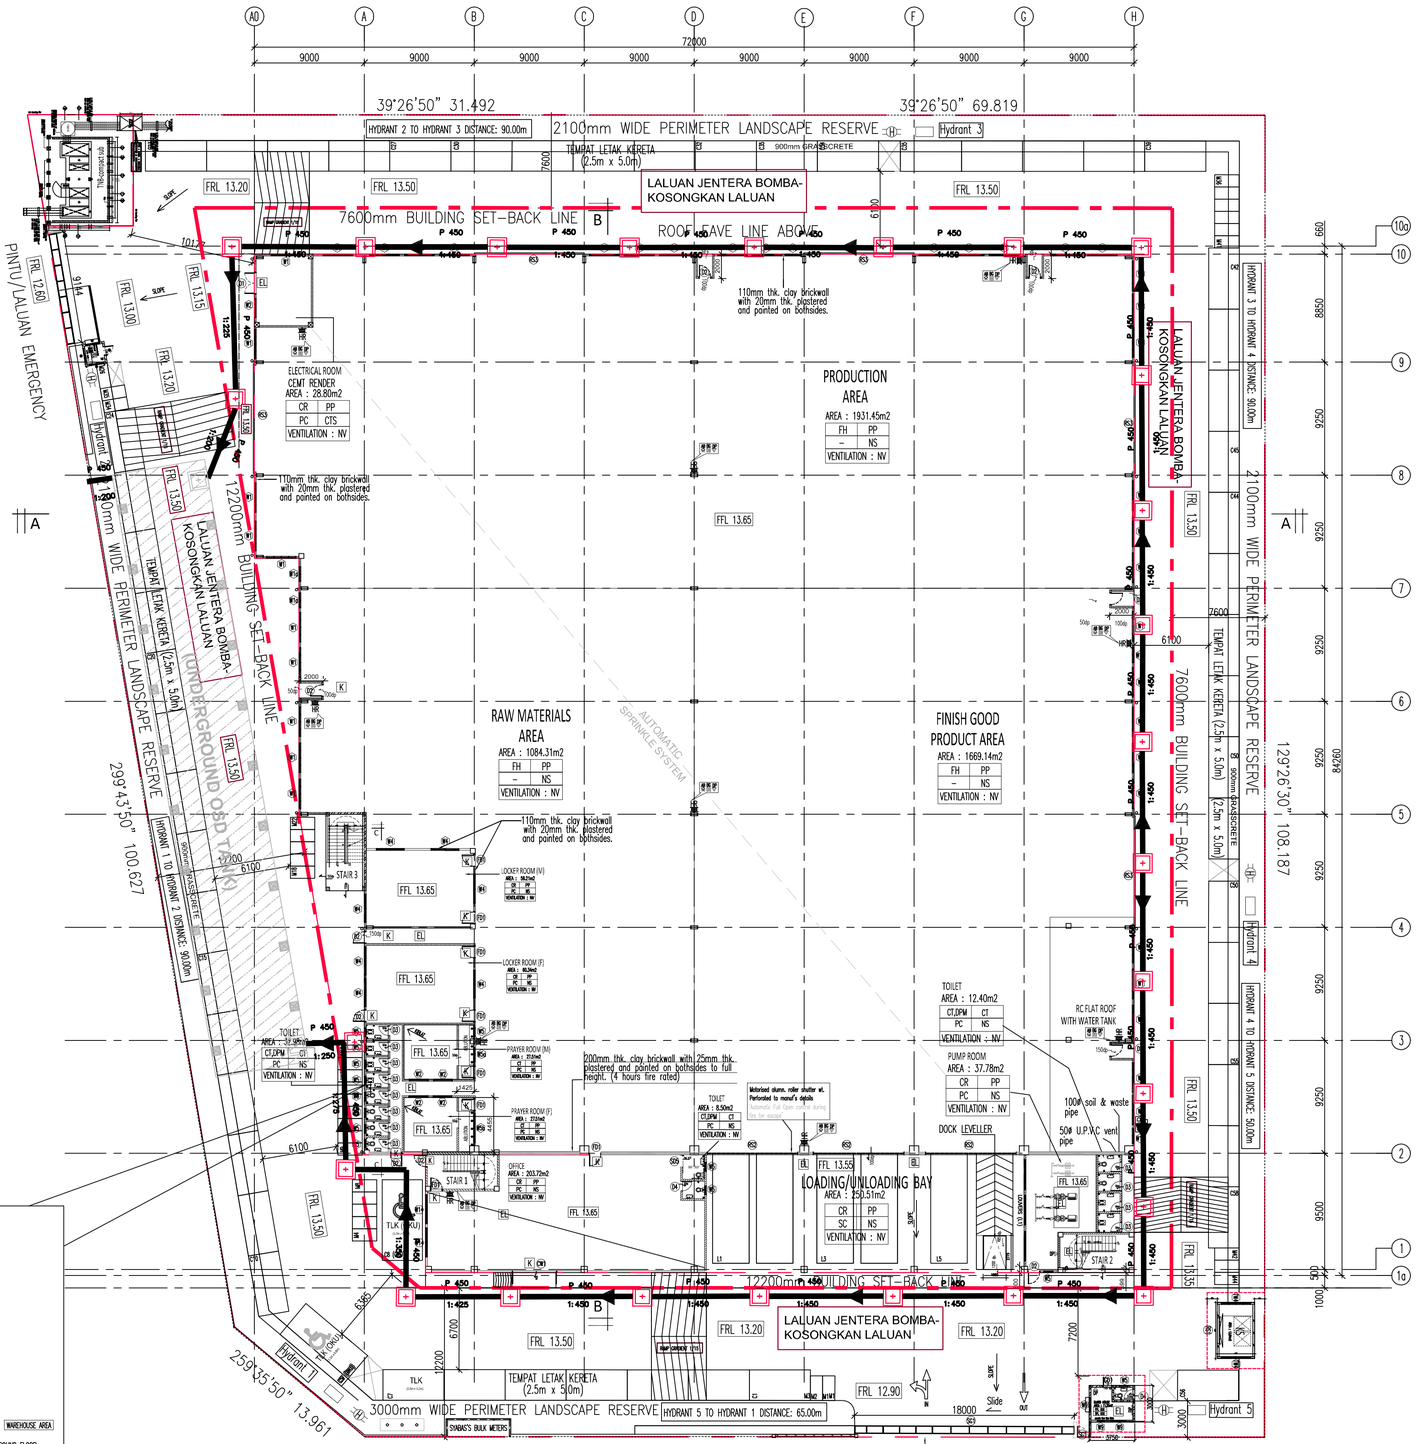

GROUND FLOOR LAYOUT PLAN

scale 1:250

CONTROLLED DOCUMENT FOR CONSTRUCTION
11 OCT 2024
PERUNDING SCCT

ARAH UTARA & KIBLAT :

KELULUSAN MAJLIS :

TANDATANGAN PEMILIK/PEMAJU :

SANDAR DEVELOPMENT SDN BHD
NAMA : MR EE JET MIN (COMPANY DIRECTOR) (445101-T)
NO. K/P : 630729–04–5649
12–1, JALAN USJ HEIGHT 1/1C,USJ AVENUE, 47610 SUBANG JAYA
SELANGOR DARUL EHSAN
Tel: 03–80810069

TANDATANGAN & NAMA JURUTERA :

PERUNDING SCCT (2097020–P)
A–08–08, Block A, Tropicana Avenue, No. 12,
Persiaran Tropicana,Tropicana Golf & Country Resort, PJU 3,
47410 Petaling Jaya, Selangor Darul Ehsan.
Tel: 016–214 3988 E: stsccconsult@gmail.com / stsccconsult@yahoo.com

IR. CHUAH SHANG CHING
(No K/P : 751229–06–5353)
"Saya memperakui bahawa perinci–perinci dalam pelan–pelan ini adalah menurut kehendak–kehendak Undang–Undang Kecil Bangunan Seragam 1986 (Selangor) dan saya setuju terima tanggungjawab penuh dengan sewajarnya".

TAJUK PERMOHONAN :

PERMOHONAN PELAN BANGUNAN BAGI CADANGAN PEMBANGUNAN PERINDUSTRIAN YANG MENGANDUNGI :–

I) 2 UNIT PONDOK PENGAWAL
II) 1 UNIT PENCAWANG ELEKTRIK
III) 1 UNIT KEBUK SAMPAH
IV) 1 UNIT KILANG (ARAS BAWAH)
V) 1 UNIT PEJABAT YANG MENGANDUNGI 2 TINGKAT (ARAS BAWAH DAN 1)
VI) 1 UNIT TEMPAT PENYIMPANAN BARANG (ARAS 2)

DI ATAS PT 41720, NO 22, JALAN TIAI 3/1/3
TAMAN INDUSTRI ALAM JAYA II , 42300 BANDAR PUNCAK ALAM, MUKIM IJOK, DAERAH KUALA SELANGOR, SELANGOR DARUL EHSAN.

UNTUK : SANDAR DEVELOPMENT SDN. BHD.
AKTIVITI PERMOHONAN : KILANG UNTUK DISEWA

CONSTRUCTION DRAWING

This Drawing is to be read in conjunction with all relevant Architect, M/E Engineers and Specialist details. The Contractor must check and confirm dimensions. No dimensions to be scaled from this drawing. Any discrepancies are to be reported to and resolved by the Engineer before work in connection with this drawing is carried out.

TAJUK LUKISAN :

WAREHOUSE
GROUND FLOOR LAYOUT PLAN

Scale	: AS SHOWN	Date	: OCT 2024
Drawn by	: SCCT	Designed by	: SCCT
Checked by	: Ir. SC Chuah	Approved by	: Ir. SC Chuah

No. Rujukan Pelan :

SCCT	SPAF	2023	A	003		

No part of the content of this drawing may be reproduced, stored or transmitted in any form or by any means, without the express written permission of Perunding SCCT (2097020–P)